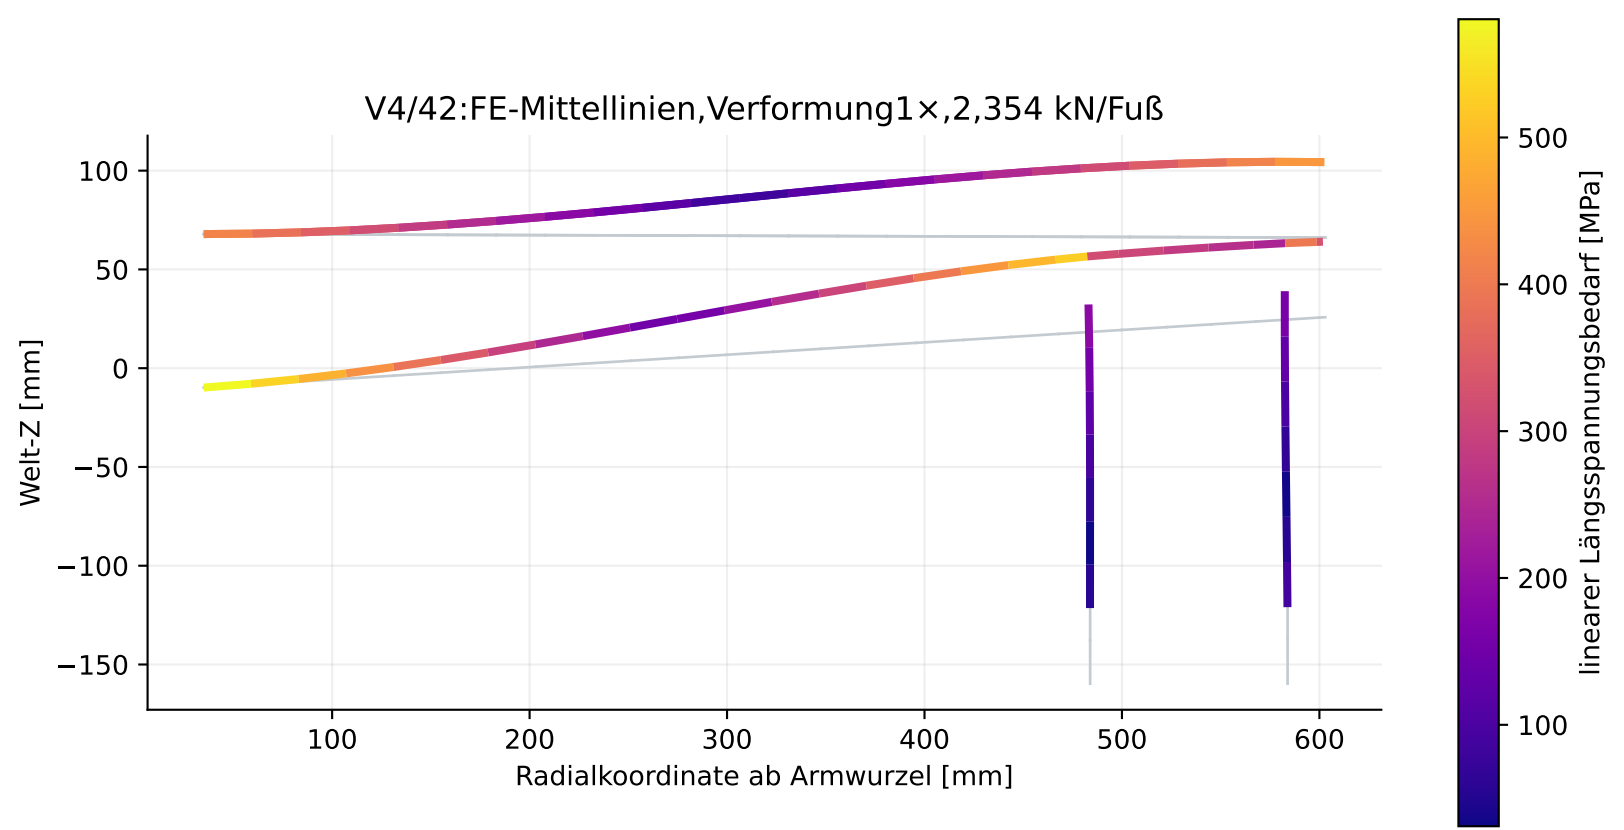

Graue Lage unverformt.Obere Rohrpaare überlagern sich in der Projektion.Keine Volumen-/Laminat-Spannungs-FEA.